


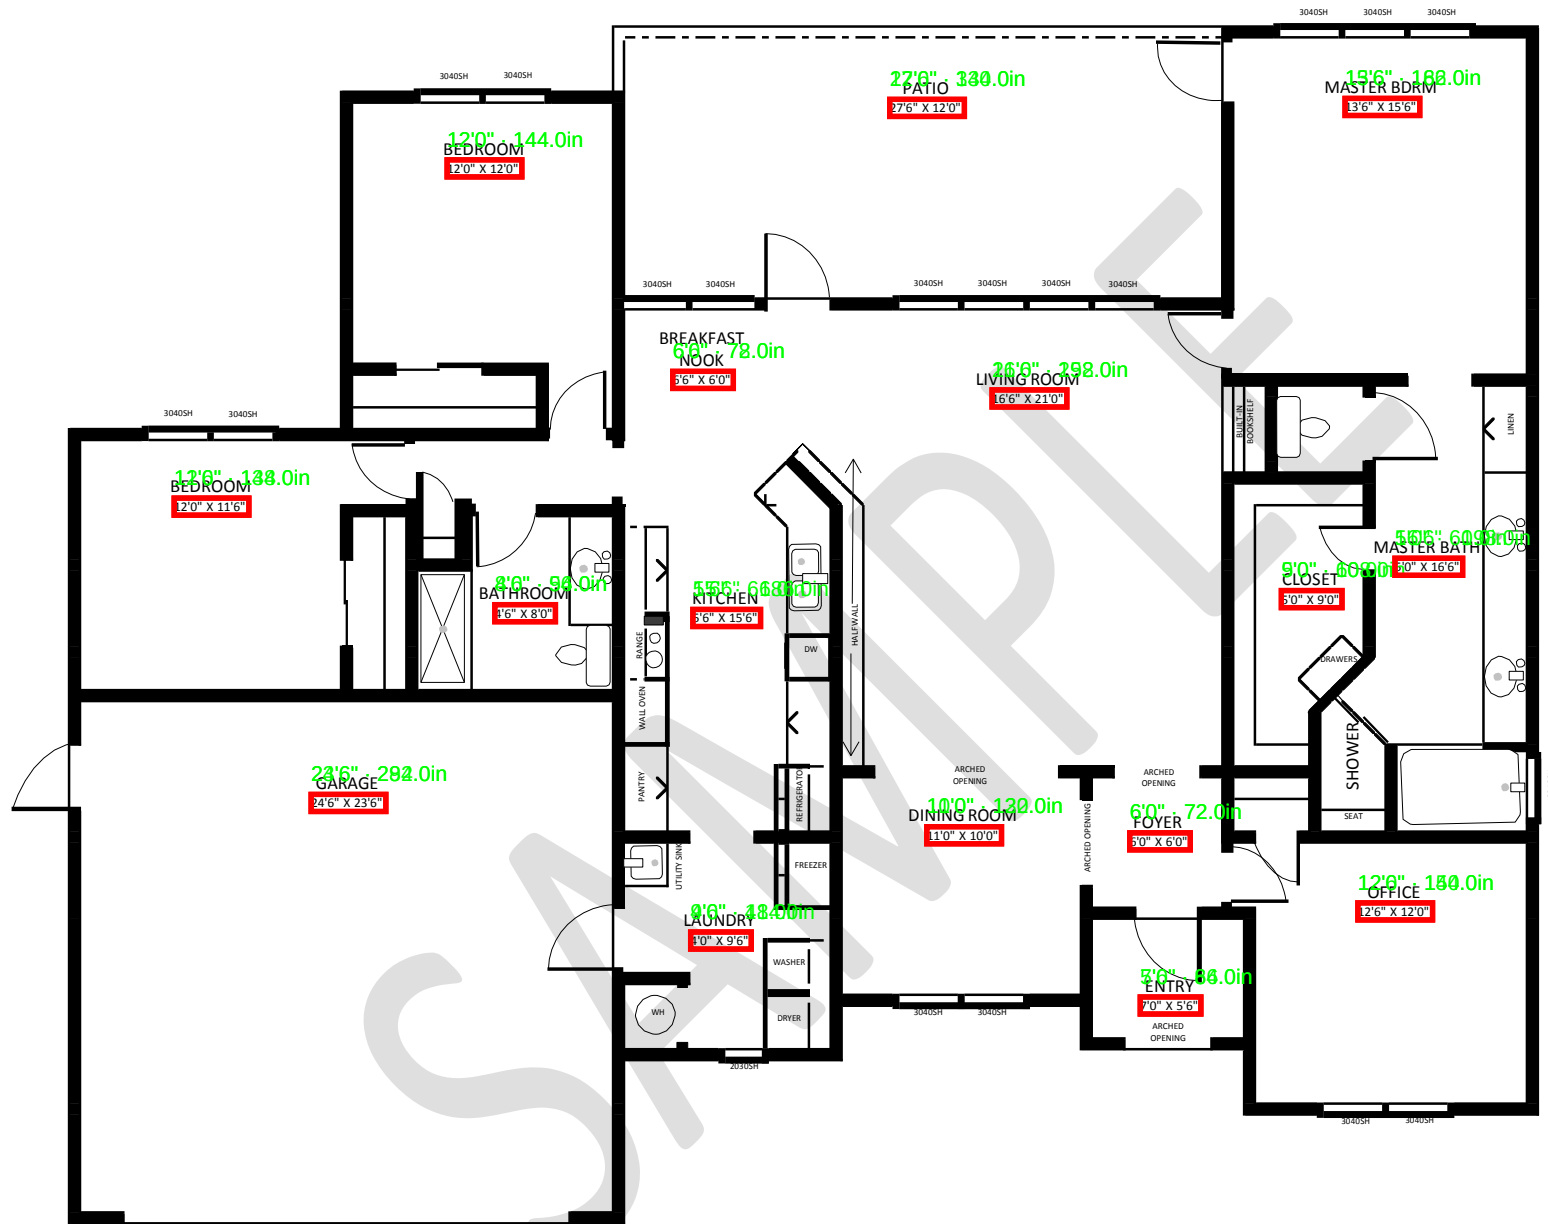

Floor Plan with all rooms, plumbing fixtures, doors, windows and dimensions or scale clearly labeled